



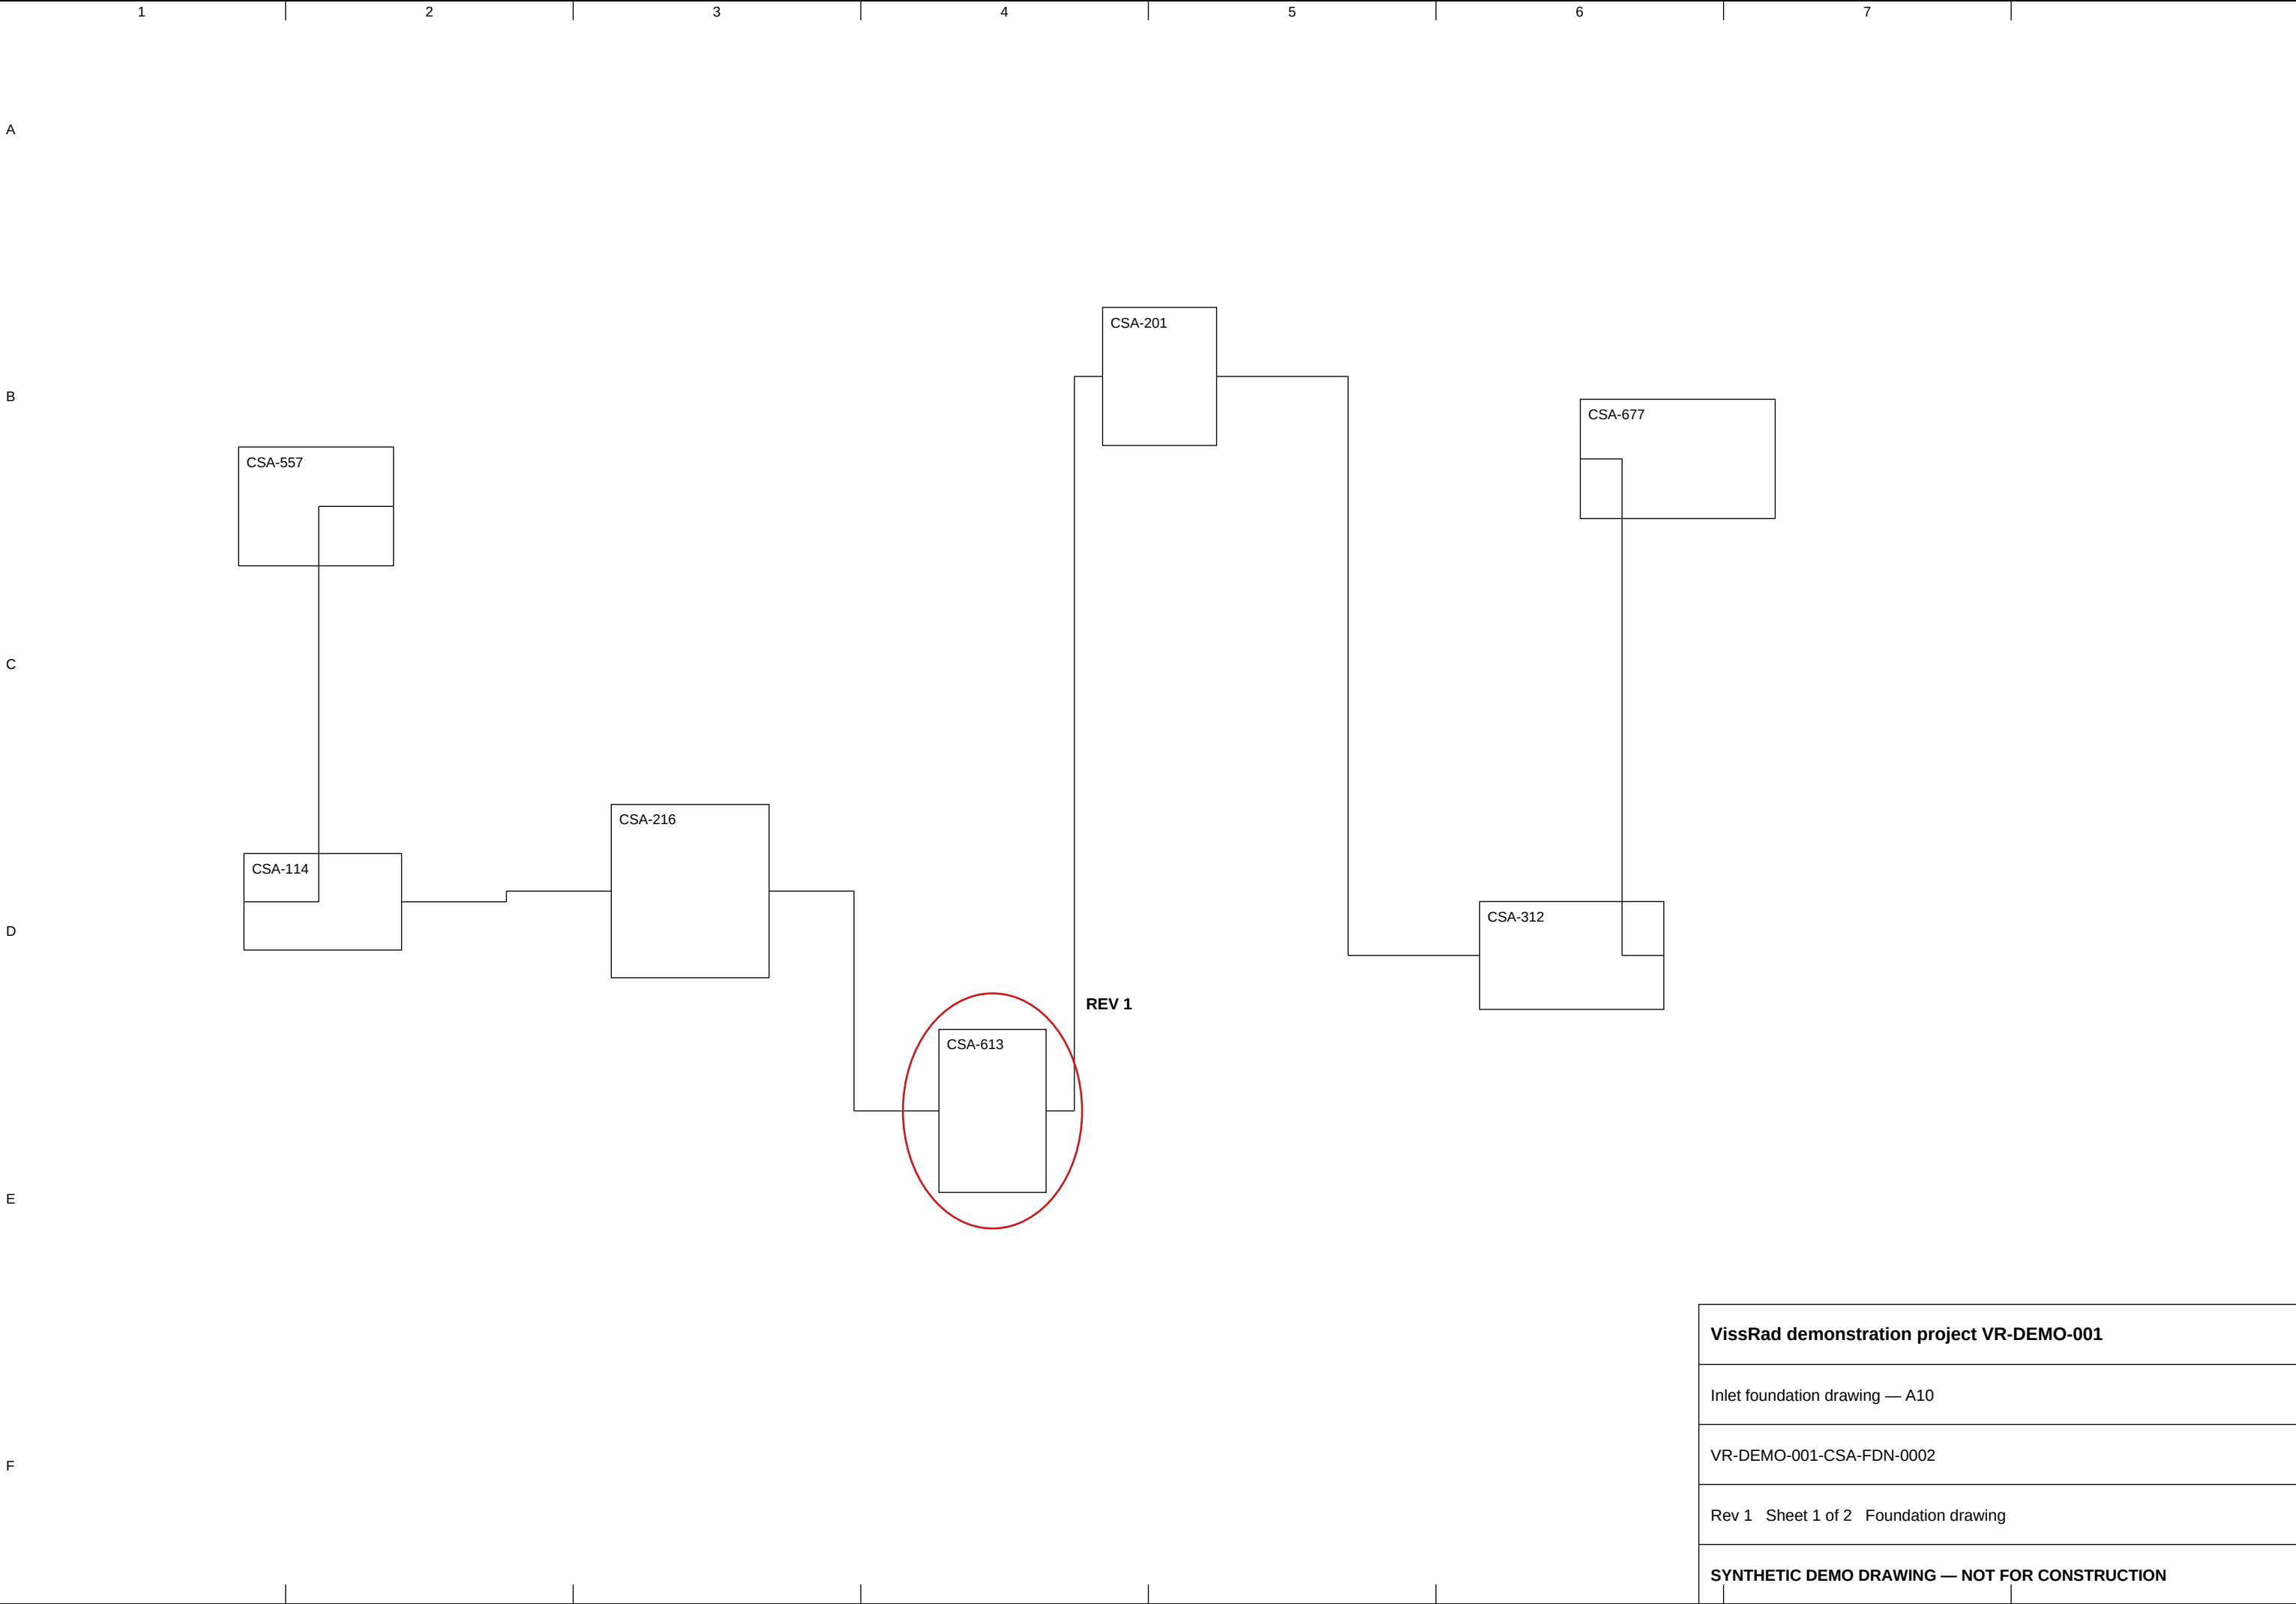

VissRad demonstration project VR-DEMO-001
Inlet foundation drawing — A10
VR-DEMO-001-CSA-FDN-0002
Rev 1 Sheet 1 of 2 Foundation drawing
SYNTHETIC DEMO DRAWING — NOT FOR CONSTRUCTION

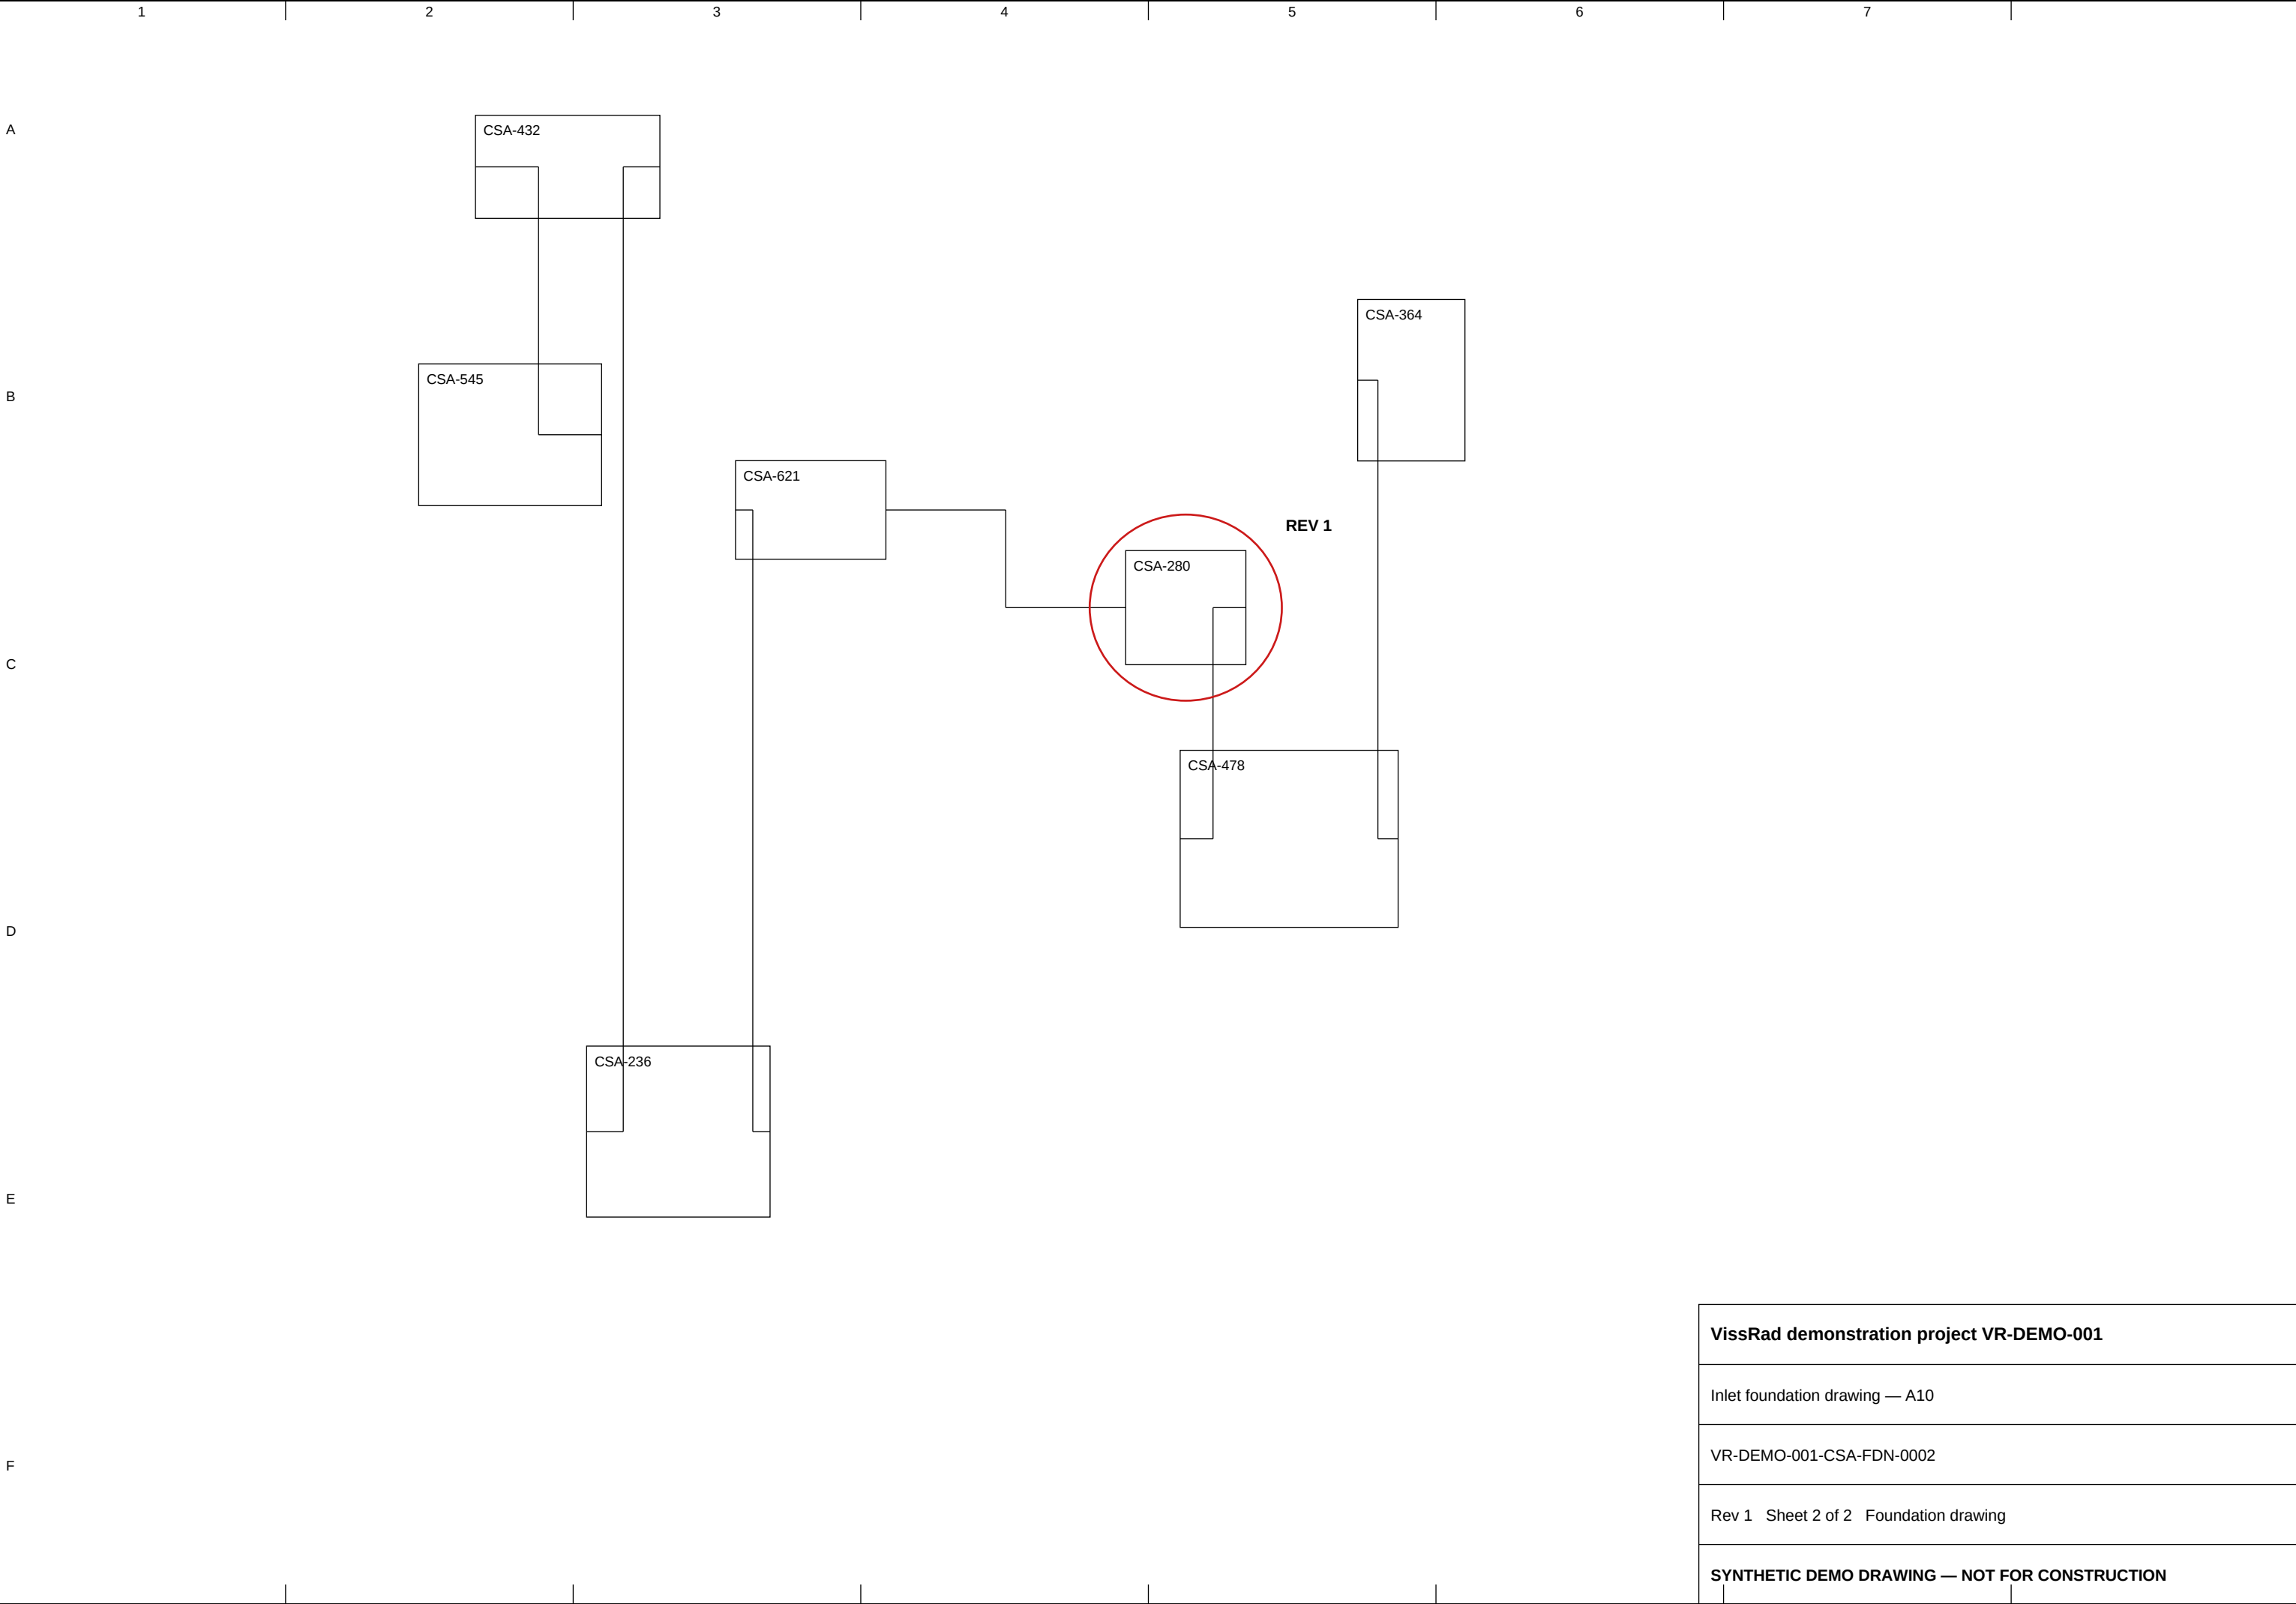

VissRad demonstration project VR-DEMO-001

Inlet foundation drawing — A10

VR-DEMO-001-CSA-FDN-0002

Rev 1 Sheet 2 of 2 Foundation drawing

SYNTHETIC DEMO DRAWING — NOT FOR CONSTRUCTION